Last Updated: 4/22/2019 10:25 AM

Field Name	Lease Name	Well No.	County	State	API No.
Long Beach	SHWU	A-37_OH	Los Angeles	California	04-037-12382-0000


Version	Version Tag	Spud Date	Comp. Date	Plug Date	GL (ft)	KB (ft)
0	A-37_OH	12/10/1926	3/1/1927		105.0	

Section	Township/Block	Range/Survey	Dist. N/S (ft)	Dir. N/S	Dist. E/W (ft)	Dir. E/W	Prior Operator/Name
19	4S	12W	4435				Italo / #3

Operator	Well Type	Well Status	Latitude	Longitude	Streets
Signal Hill Petroleum		Idle	33.812083	-118.178438	Spring & California

Status Date	OH Logs	Cased Logs	Survey Logs
5/1/1976			Temp: 11/18/2009

Last Updated	Additional Information
04/22/2019 10:25 AM	

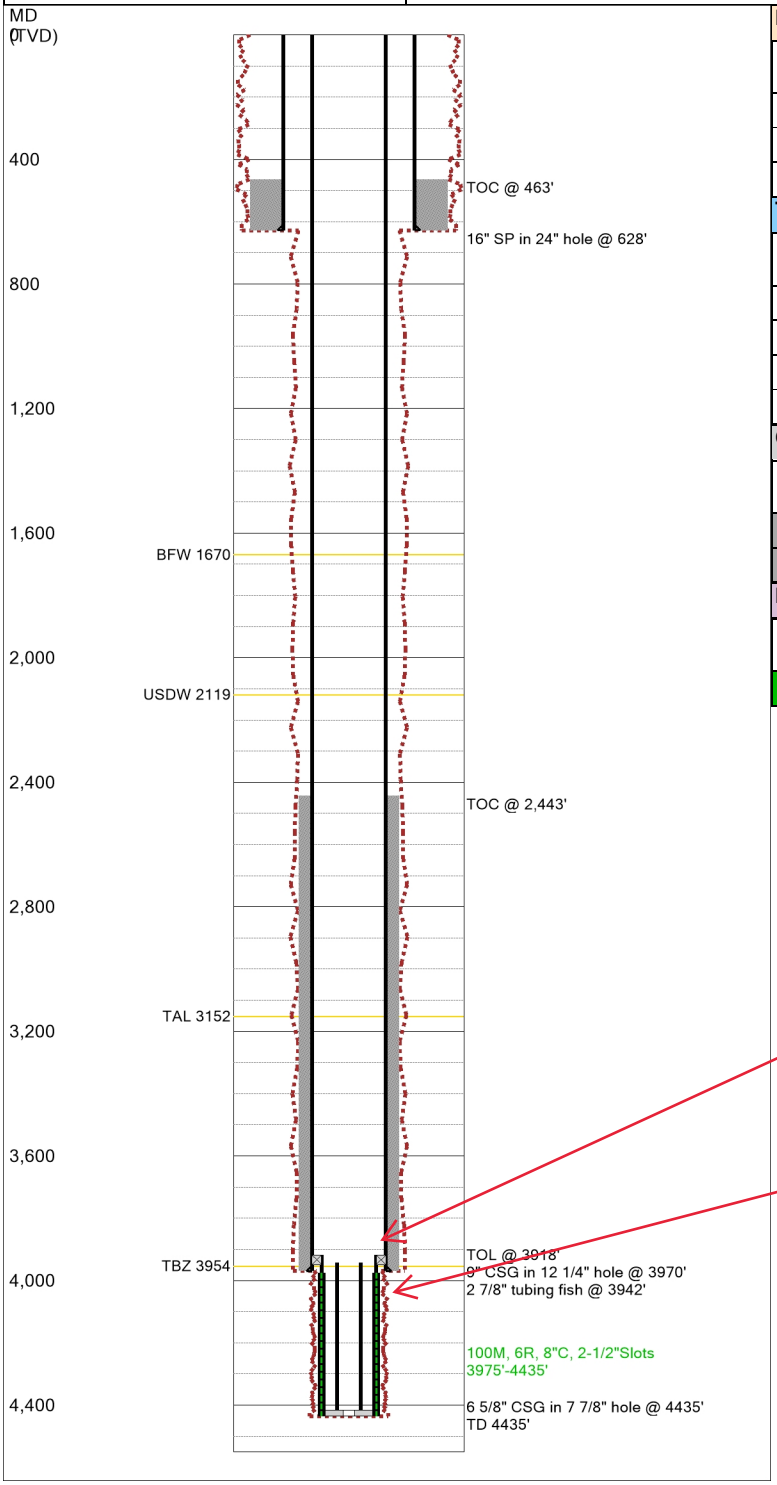

Hole Summary

Date	O.D. (in)	Top (MD ft)	Bottom (MD ft)	Memo
	24.000	0	628	
	12.250	628	3,970	
	7.875	3,970	4,435	

Tubular Summary

Date	Description	O.D. (in)	Wt (lb/ft)	Grade	Top (MD ft)	Bottom (MD ft)
	Surface Casing	16.000	68.00		0	628
	Intermediate Casing	9.000	40.00		0	3,970
	Liner	6.625	16.00		3,918	4,435
	Tubing Fish	2.875			3,942	4,435

Casing Cement Summary

C	Date	No. Sx	Csg. O.D. (in)	Top (MD ft)	Bottom (MD ft)	Memo
		500	9.000	2,443	3,970	
		250	16.000	463	628	

Perforation Summary

C	Date	Perf. Status	Formation	OA Top (MD ft)	OA Bottom (MD ft)
		Slotted		3,975	4,435

P-test 3818'-3918' in 9" 40# csg
(above TOL)

Cleanout 4000' or below
(use something that will fit in 2-7/8" tbg,
same gauge as coiled tbg we could use to
abandon the well).