
Well No: FJ-030_0

API #: 04-037-02286-00
Operator: Tidelands Oil Prod. Co.
Lease: Tidelands Field: Wilmington
Sec. 11, T 05S, R 13W, S.B.
Mat Elevation: 15.25' asl KB: 24.55' asl
Total Depth: 3703'
Directionally Drilled: Yes

Hole Sizes	Depths
17"	0'-355'
12"	355'-1470'
22"	1470'-1495'
30"	1495'-1705'
22"	1705'-1730'
12"	1730'-3655'
16"	3655'-3702'
7-5/8"	3702'-3703'

History Notes

OH Completed 11/28/50 as Upper Terminal zone producer
Well name changed from J-030 to FJ-030 11/25/83
Plugged below 3540' 01/25/84
8-5/8" csg perforated 01/25/84
Converted to Upper Terminal injector 01/25/84
Active as of 08/01/2017
Perfs Added 1/29/2020

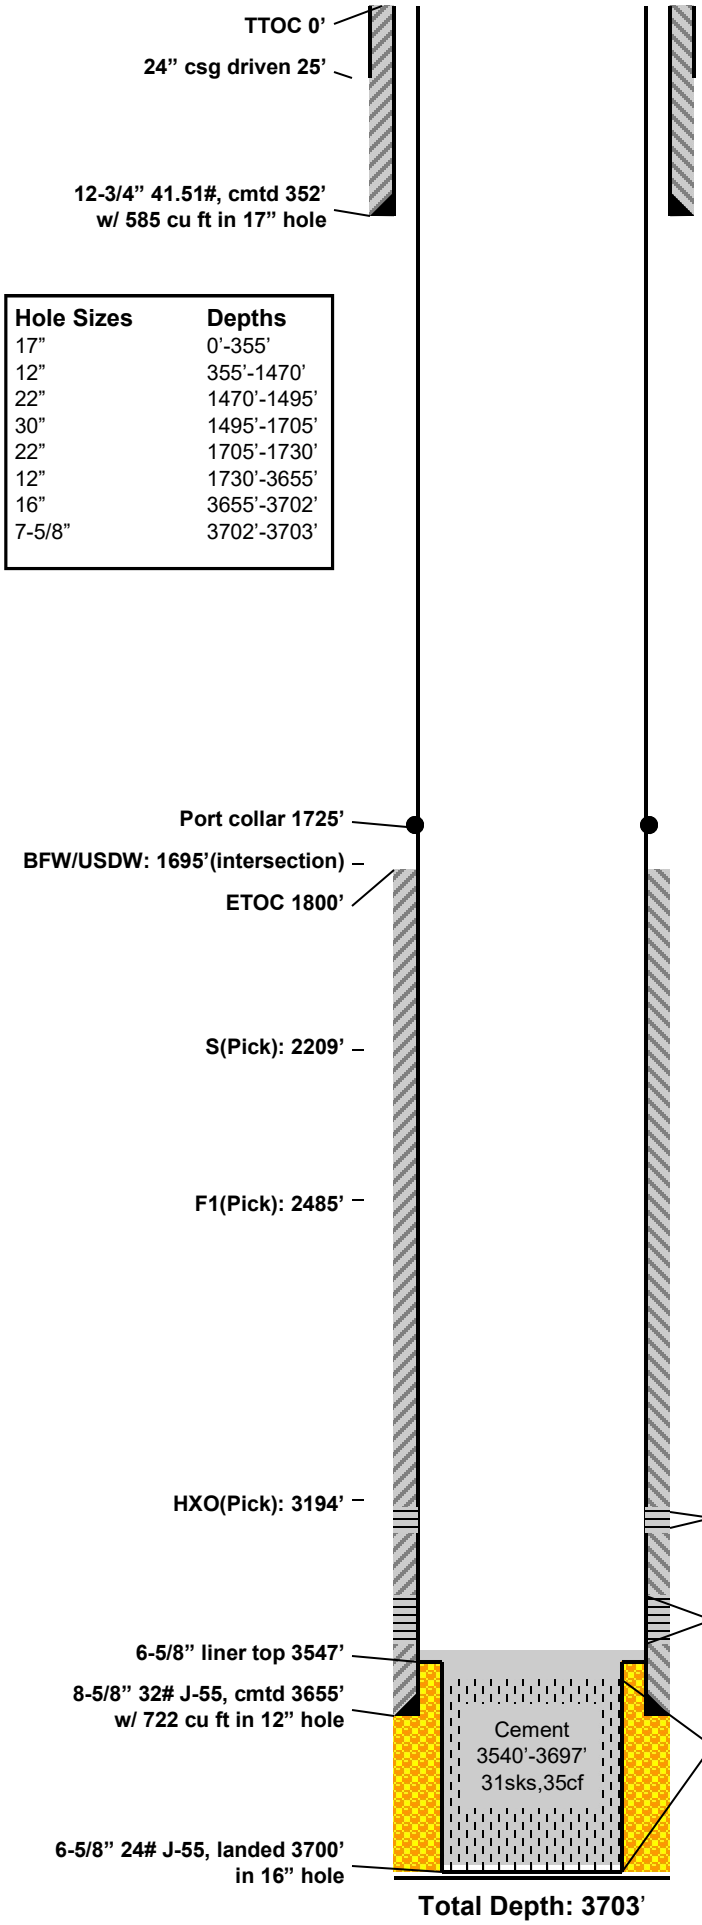

8-5/8" csg perforated w/ 1, 1/4" SPF 3194'-3195', 3212'-3232, 3242-3262', 3285'-3290' (1/2020)

8-5/8" csg perforated w/ 2, 3/8" HPF 3446'-3494', 3495'-3536' (01/1984)

6-5/8" liner slotted 3569'-3654' (2" X 45M, 4R, 48"C) & 3659'-3700' (2" X 45M, 24R, 6"C) gravel packed w/ 60 cu ft 6-8

Prepared by GEG 04/18/11

Modified by JRR 03/21/12
Modified by NP 08/01/2017
Modified by KS 4/23/2020